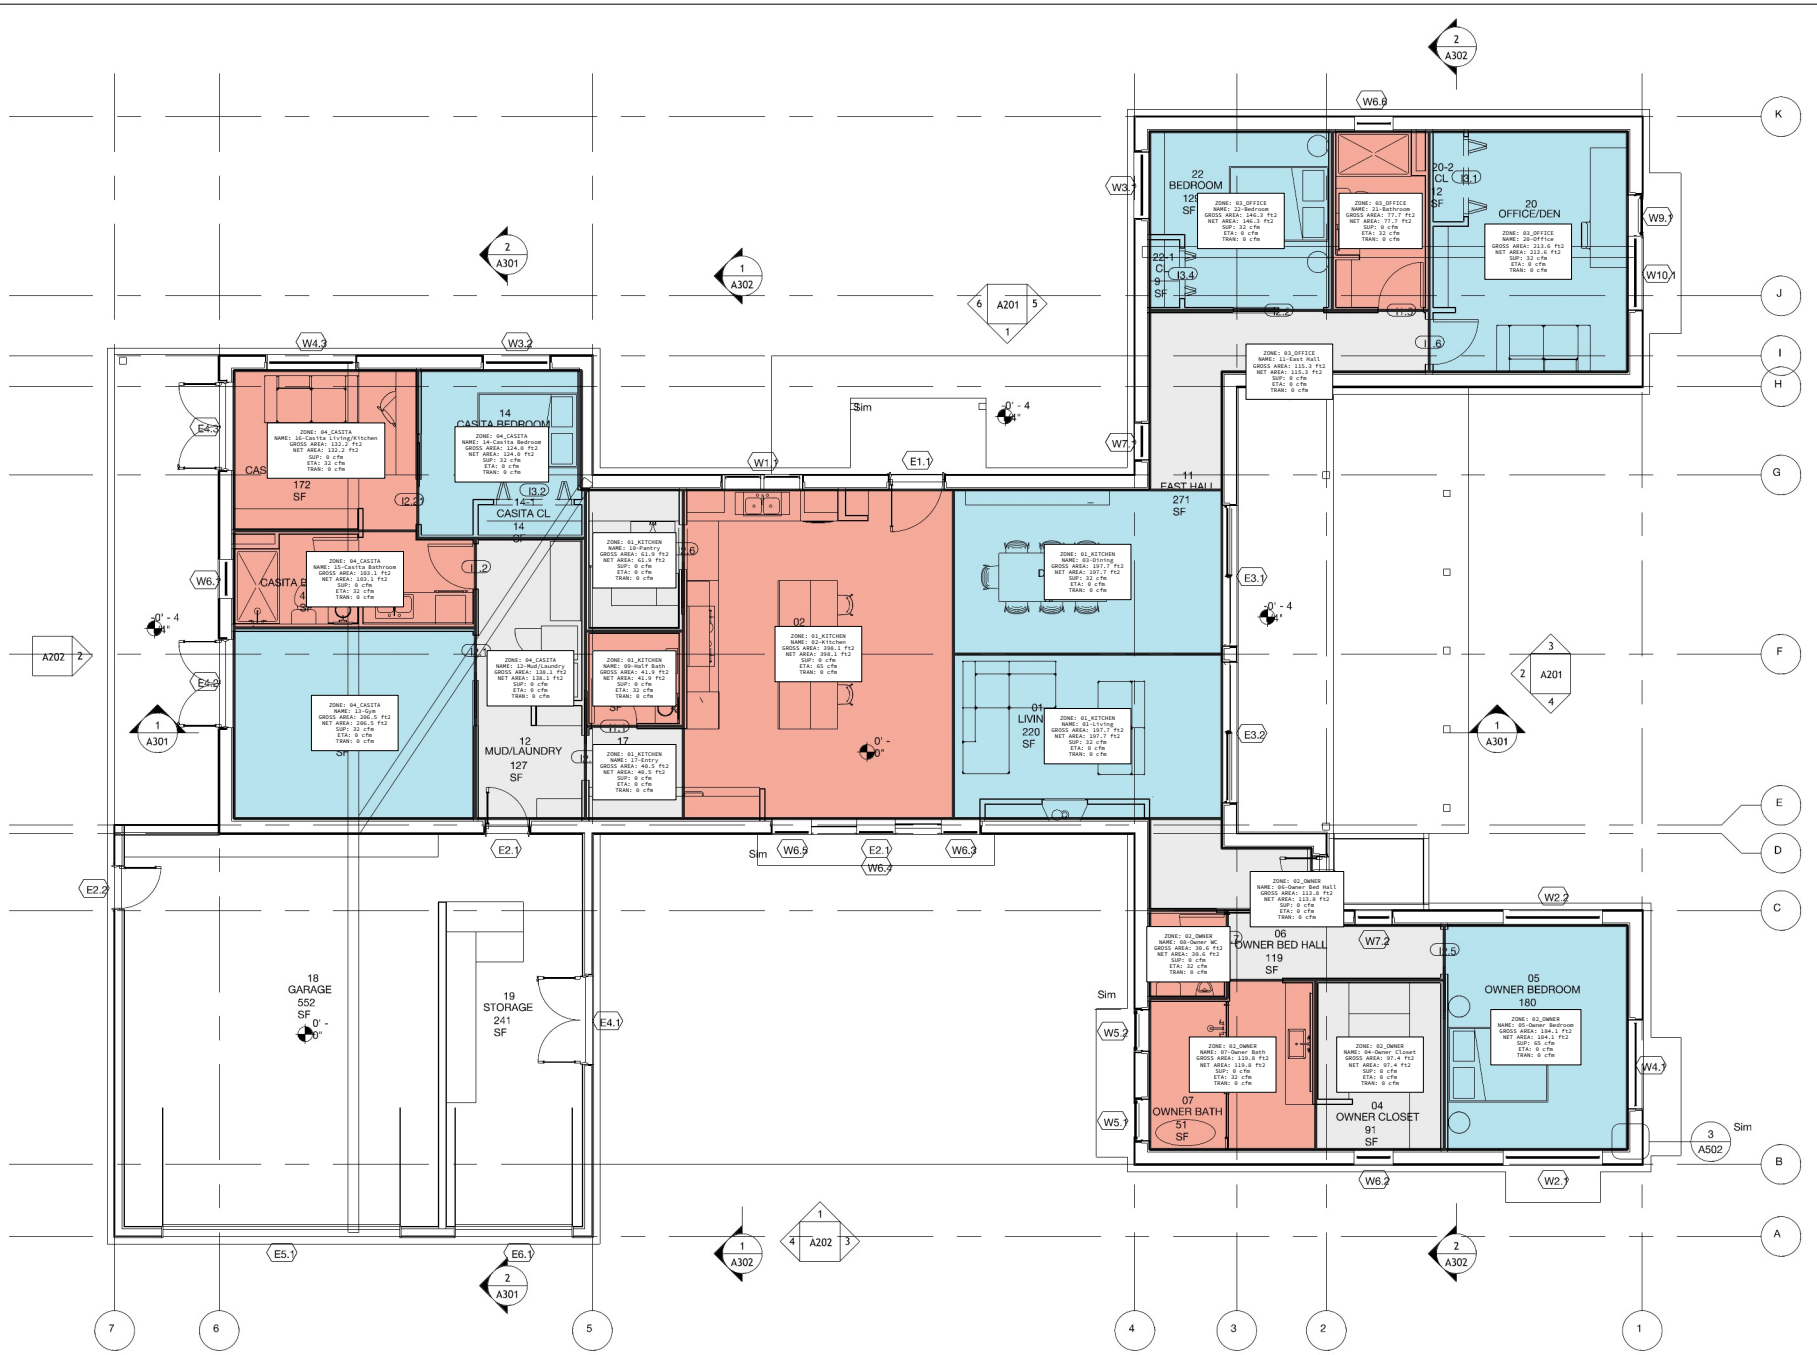

TANO ROAD HOME

FRESH-AIR VENTILATION PLANS

Ventilation:

SUPPLY | EXTRACT | SUP & ETA

August 5, 2026